



1-A تفصيلة

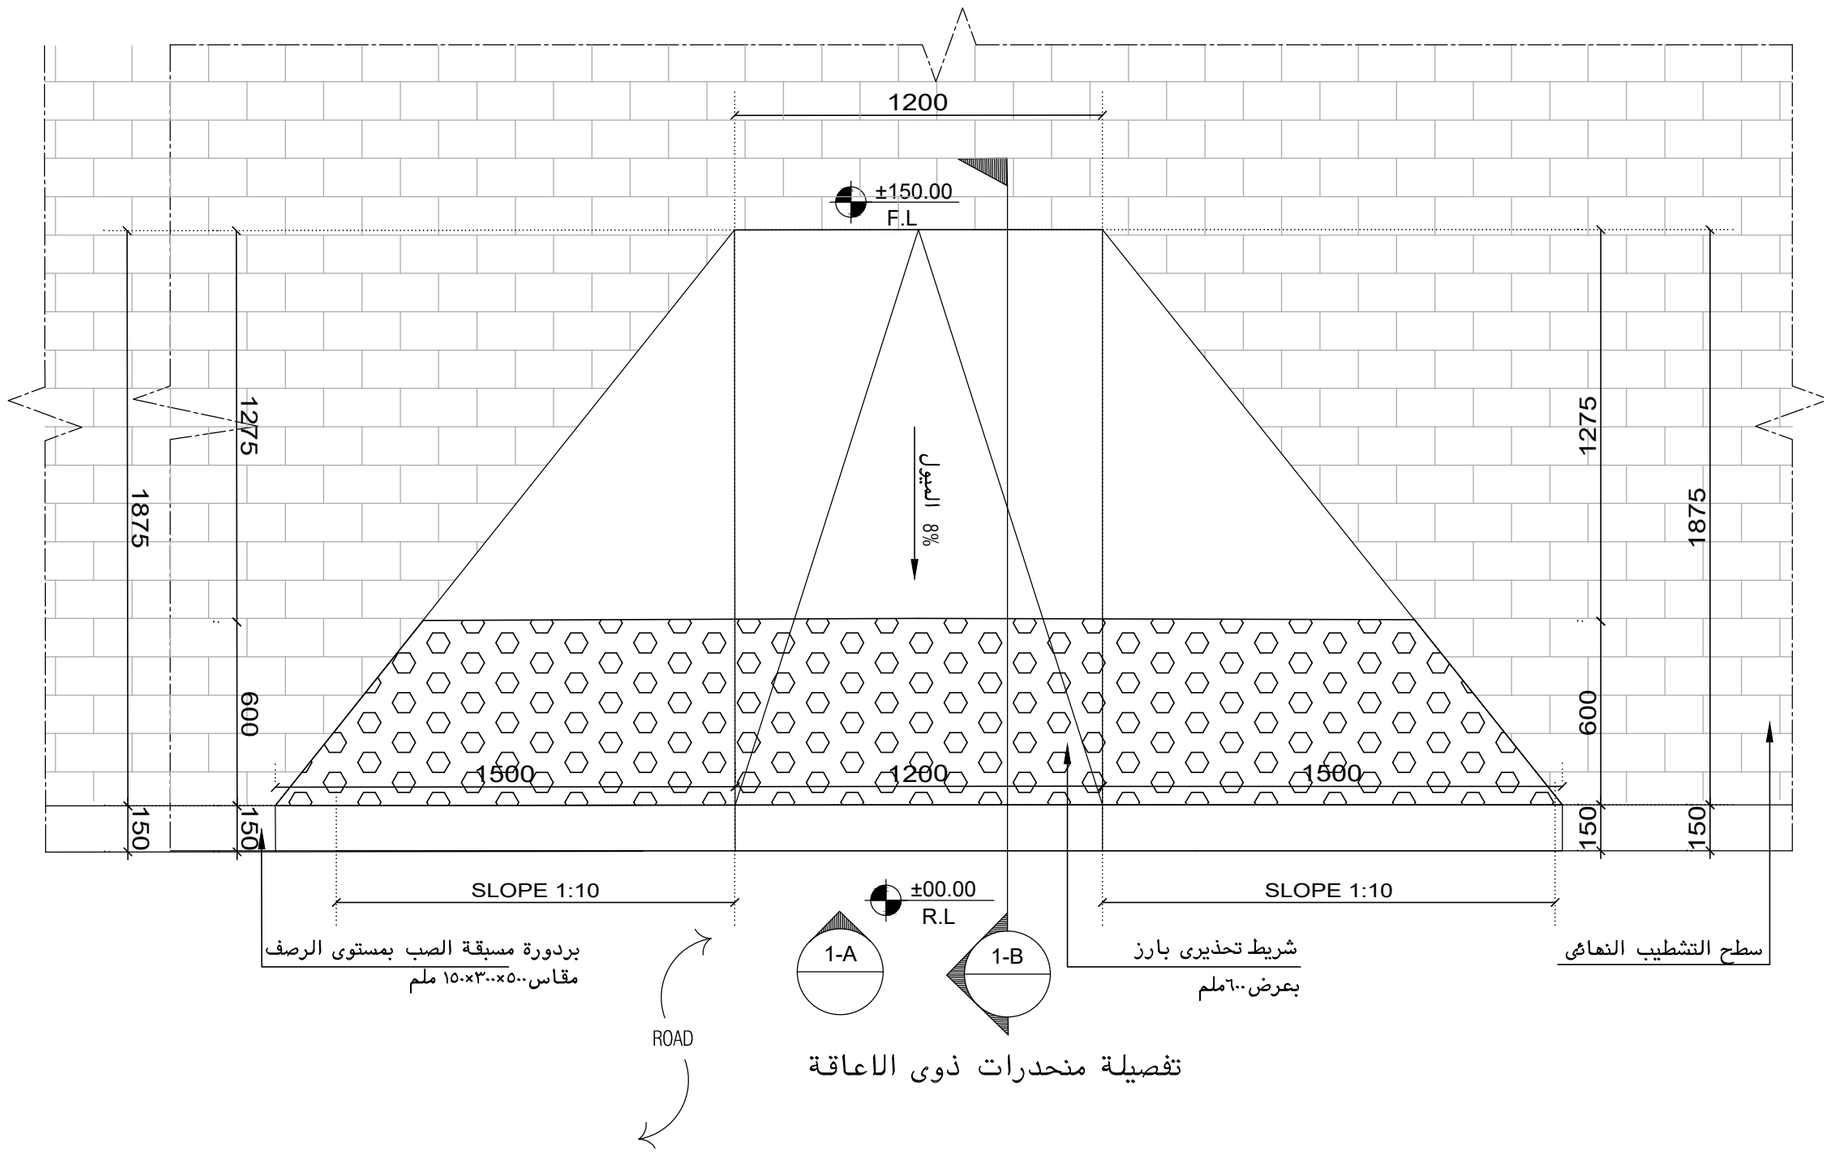


تفصيلة منحدرات ذوى الاعاقة