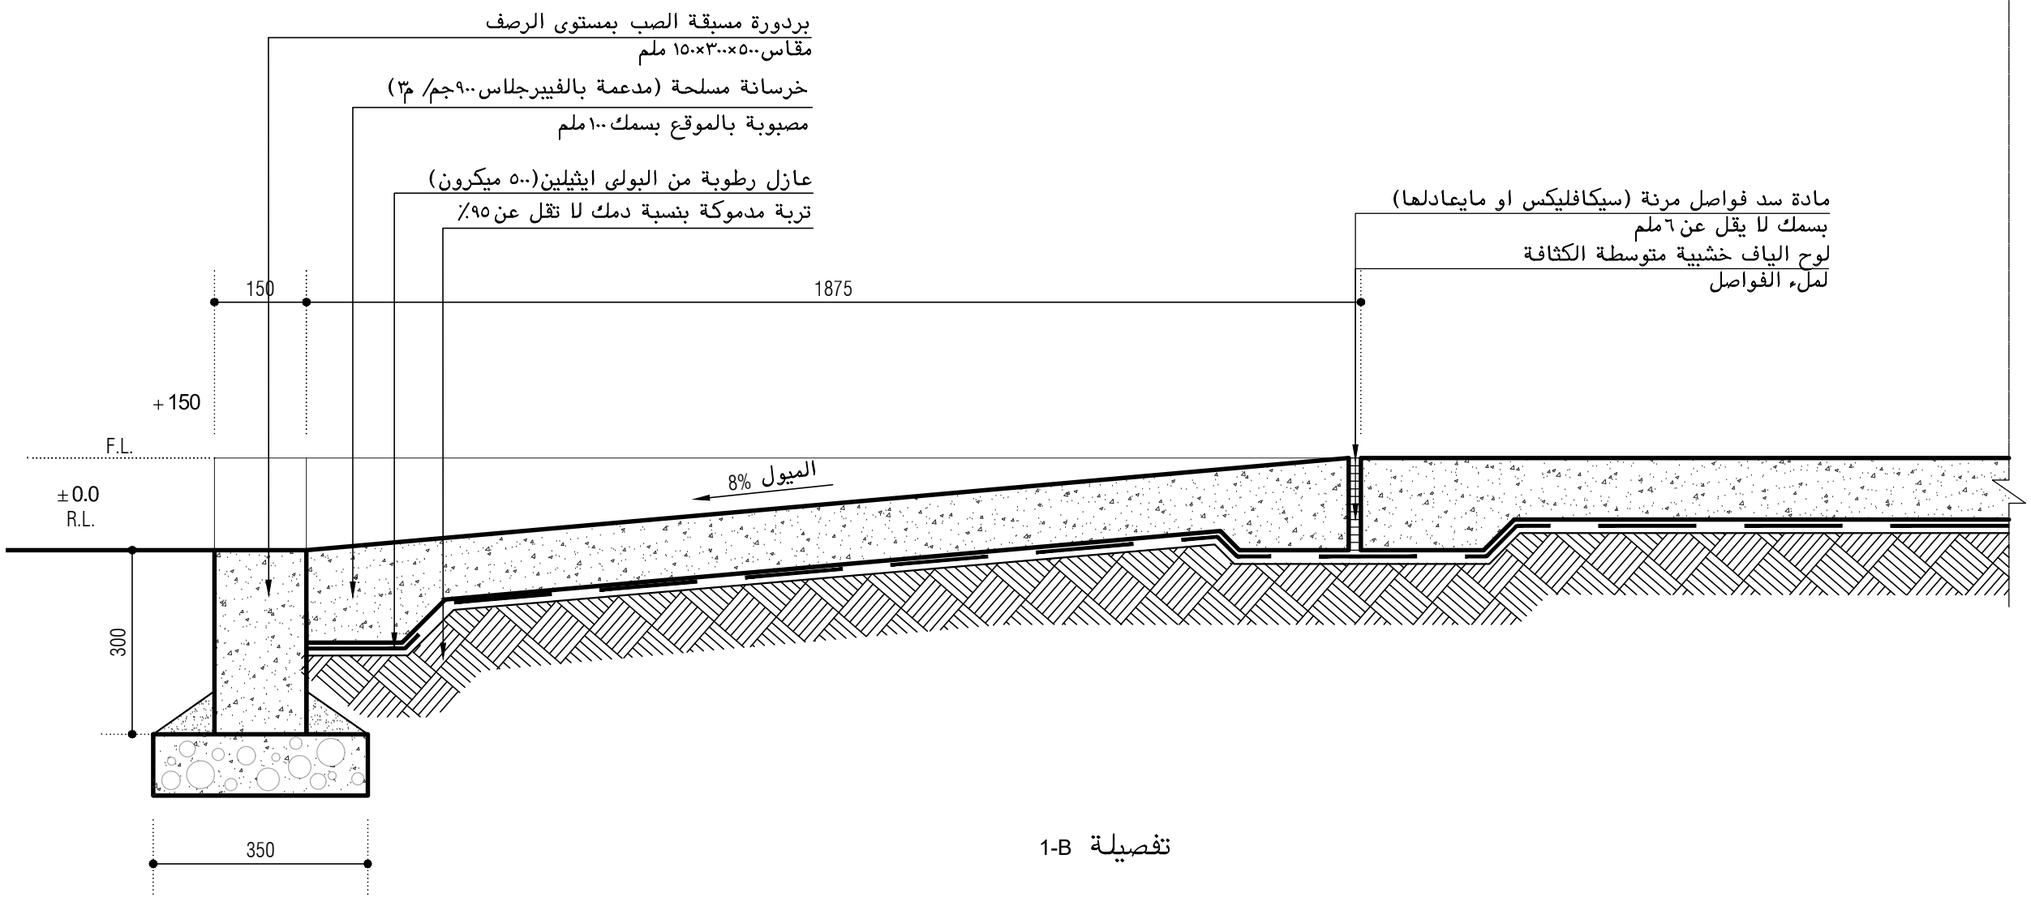

بردورة مسبقة الصب بمستوى الرصف
مقاس٥٠٠×٣٠٠×١٥٠ ملم
خرسانة مسلحة (مدعمة بالفيبرجلاس٩٠٠جم/ م٣)
مصبوبة بالموقع بسمك١٠٠ملم
عازل رطوبة من البولى ايثيلين(٥٠٠ ميكرون)
تربة مدموكة بنسبة دمك لا تقل عن٩٥٪
مادة سد فواصل مرنة (سيكافليكس او مايعادلها)
بسمك لا يقل عن٦ملم
لوح الياف خشبية متوسطة الكثافة
لملء الفواصل
150
1875
+150
F.L.
±0.0
R.L.
الميول 8%
300
350

تفصيلة 1-B