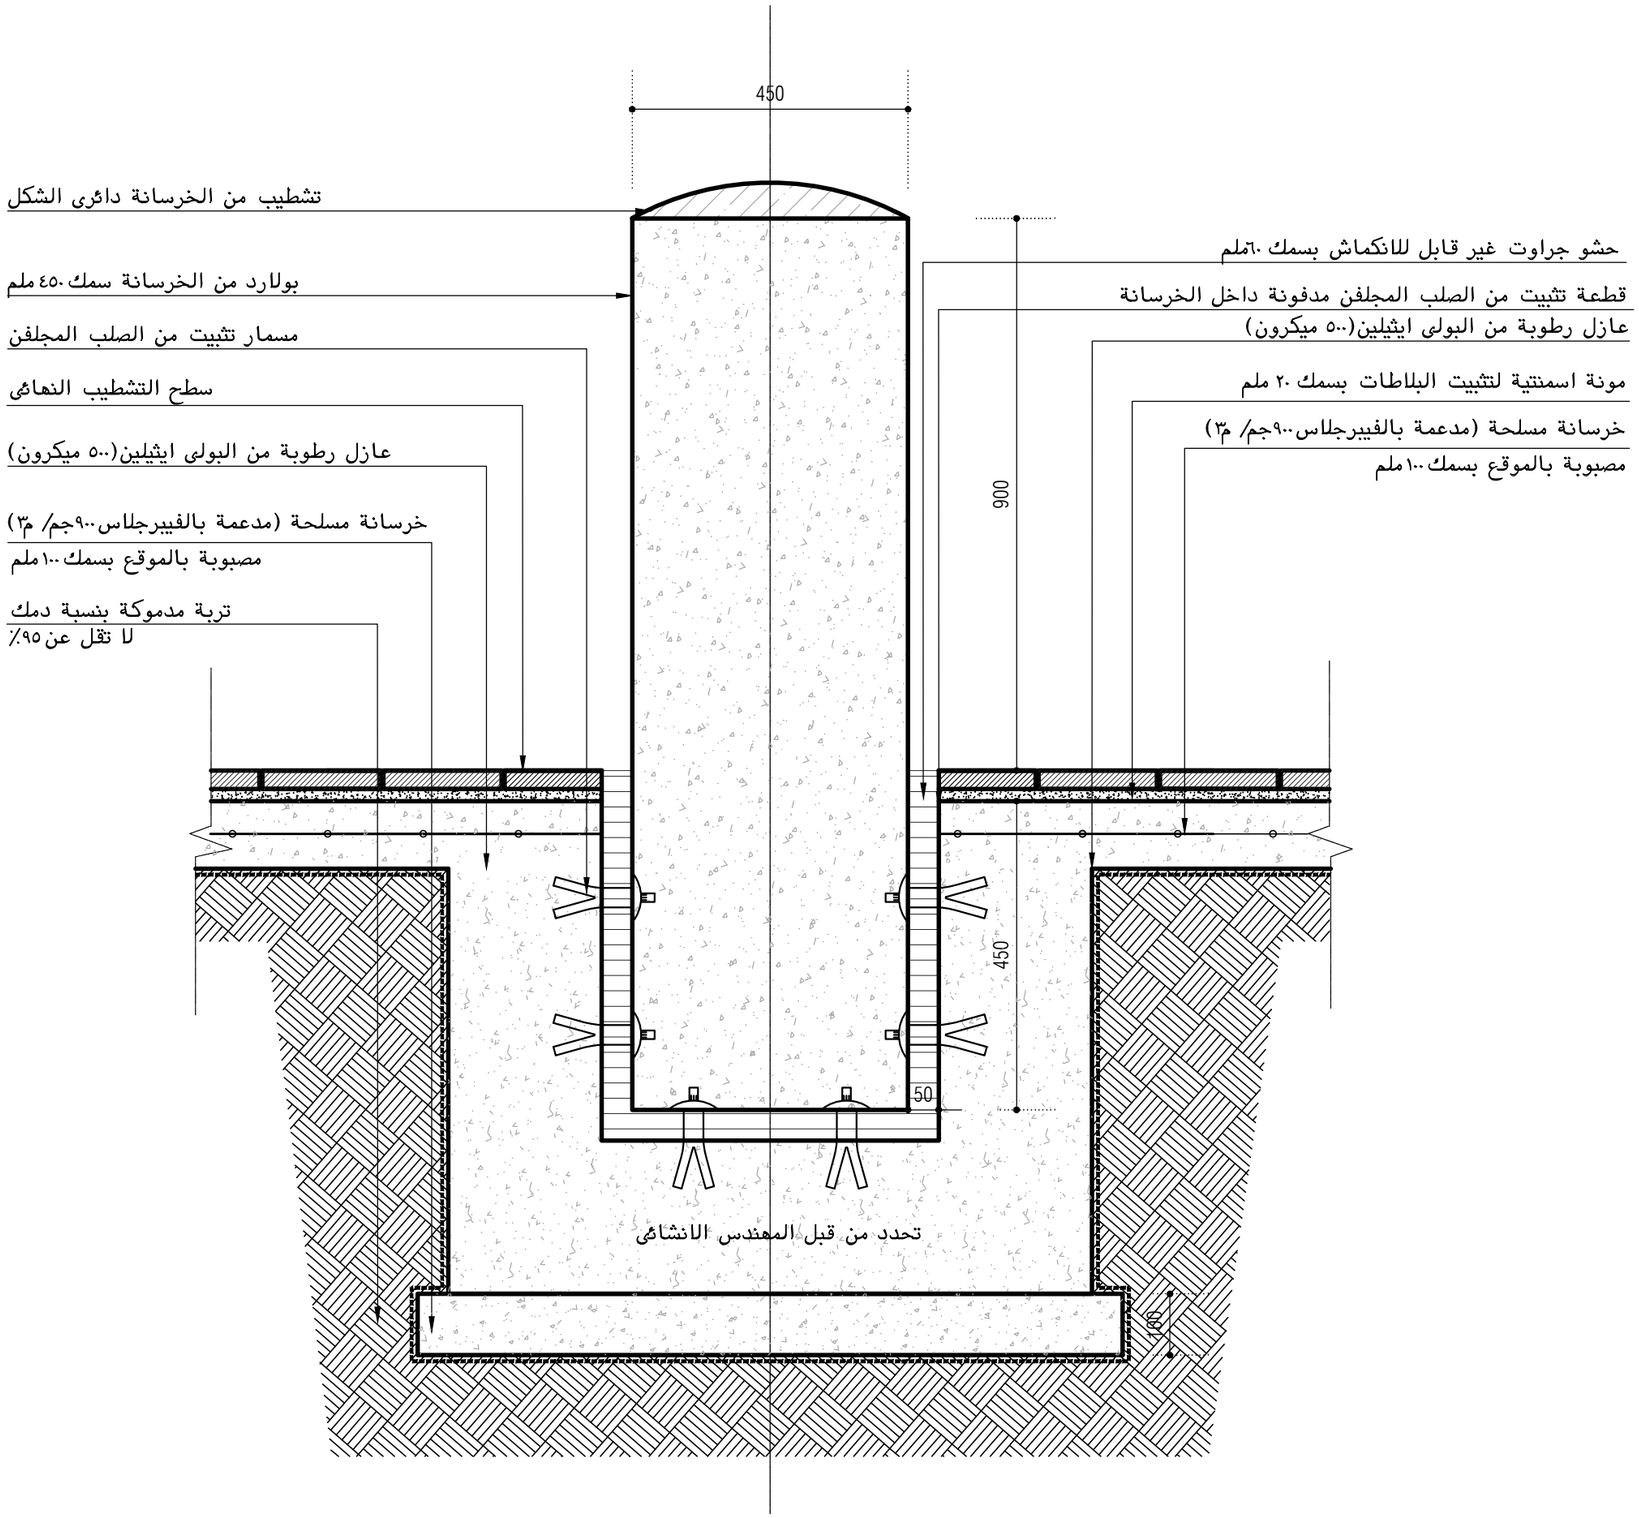


تفصيلة بولارد خرسانى